
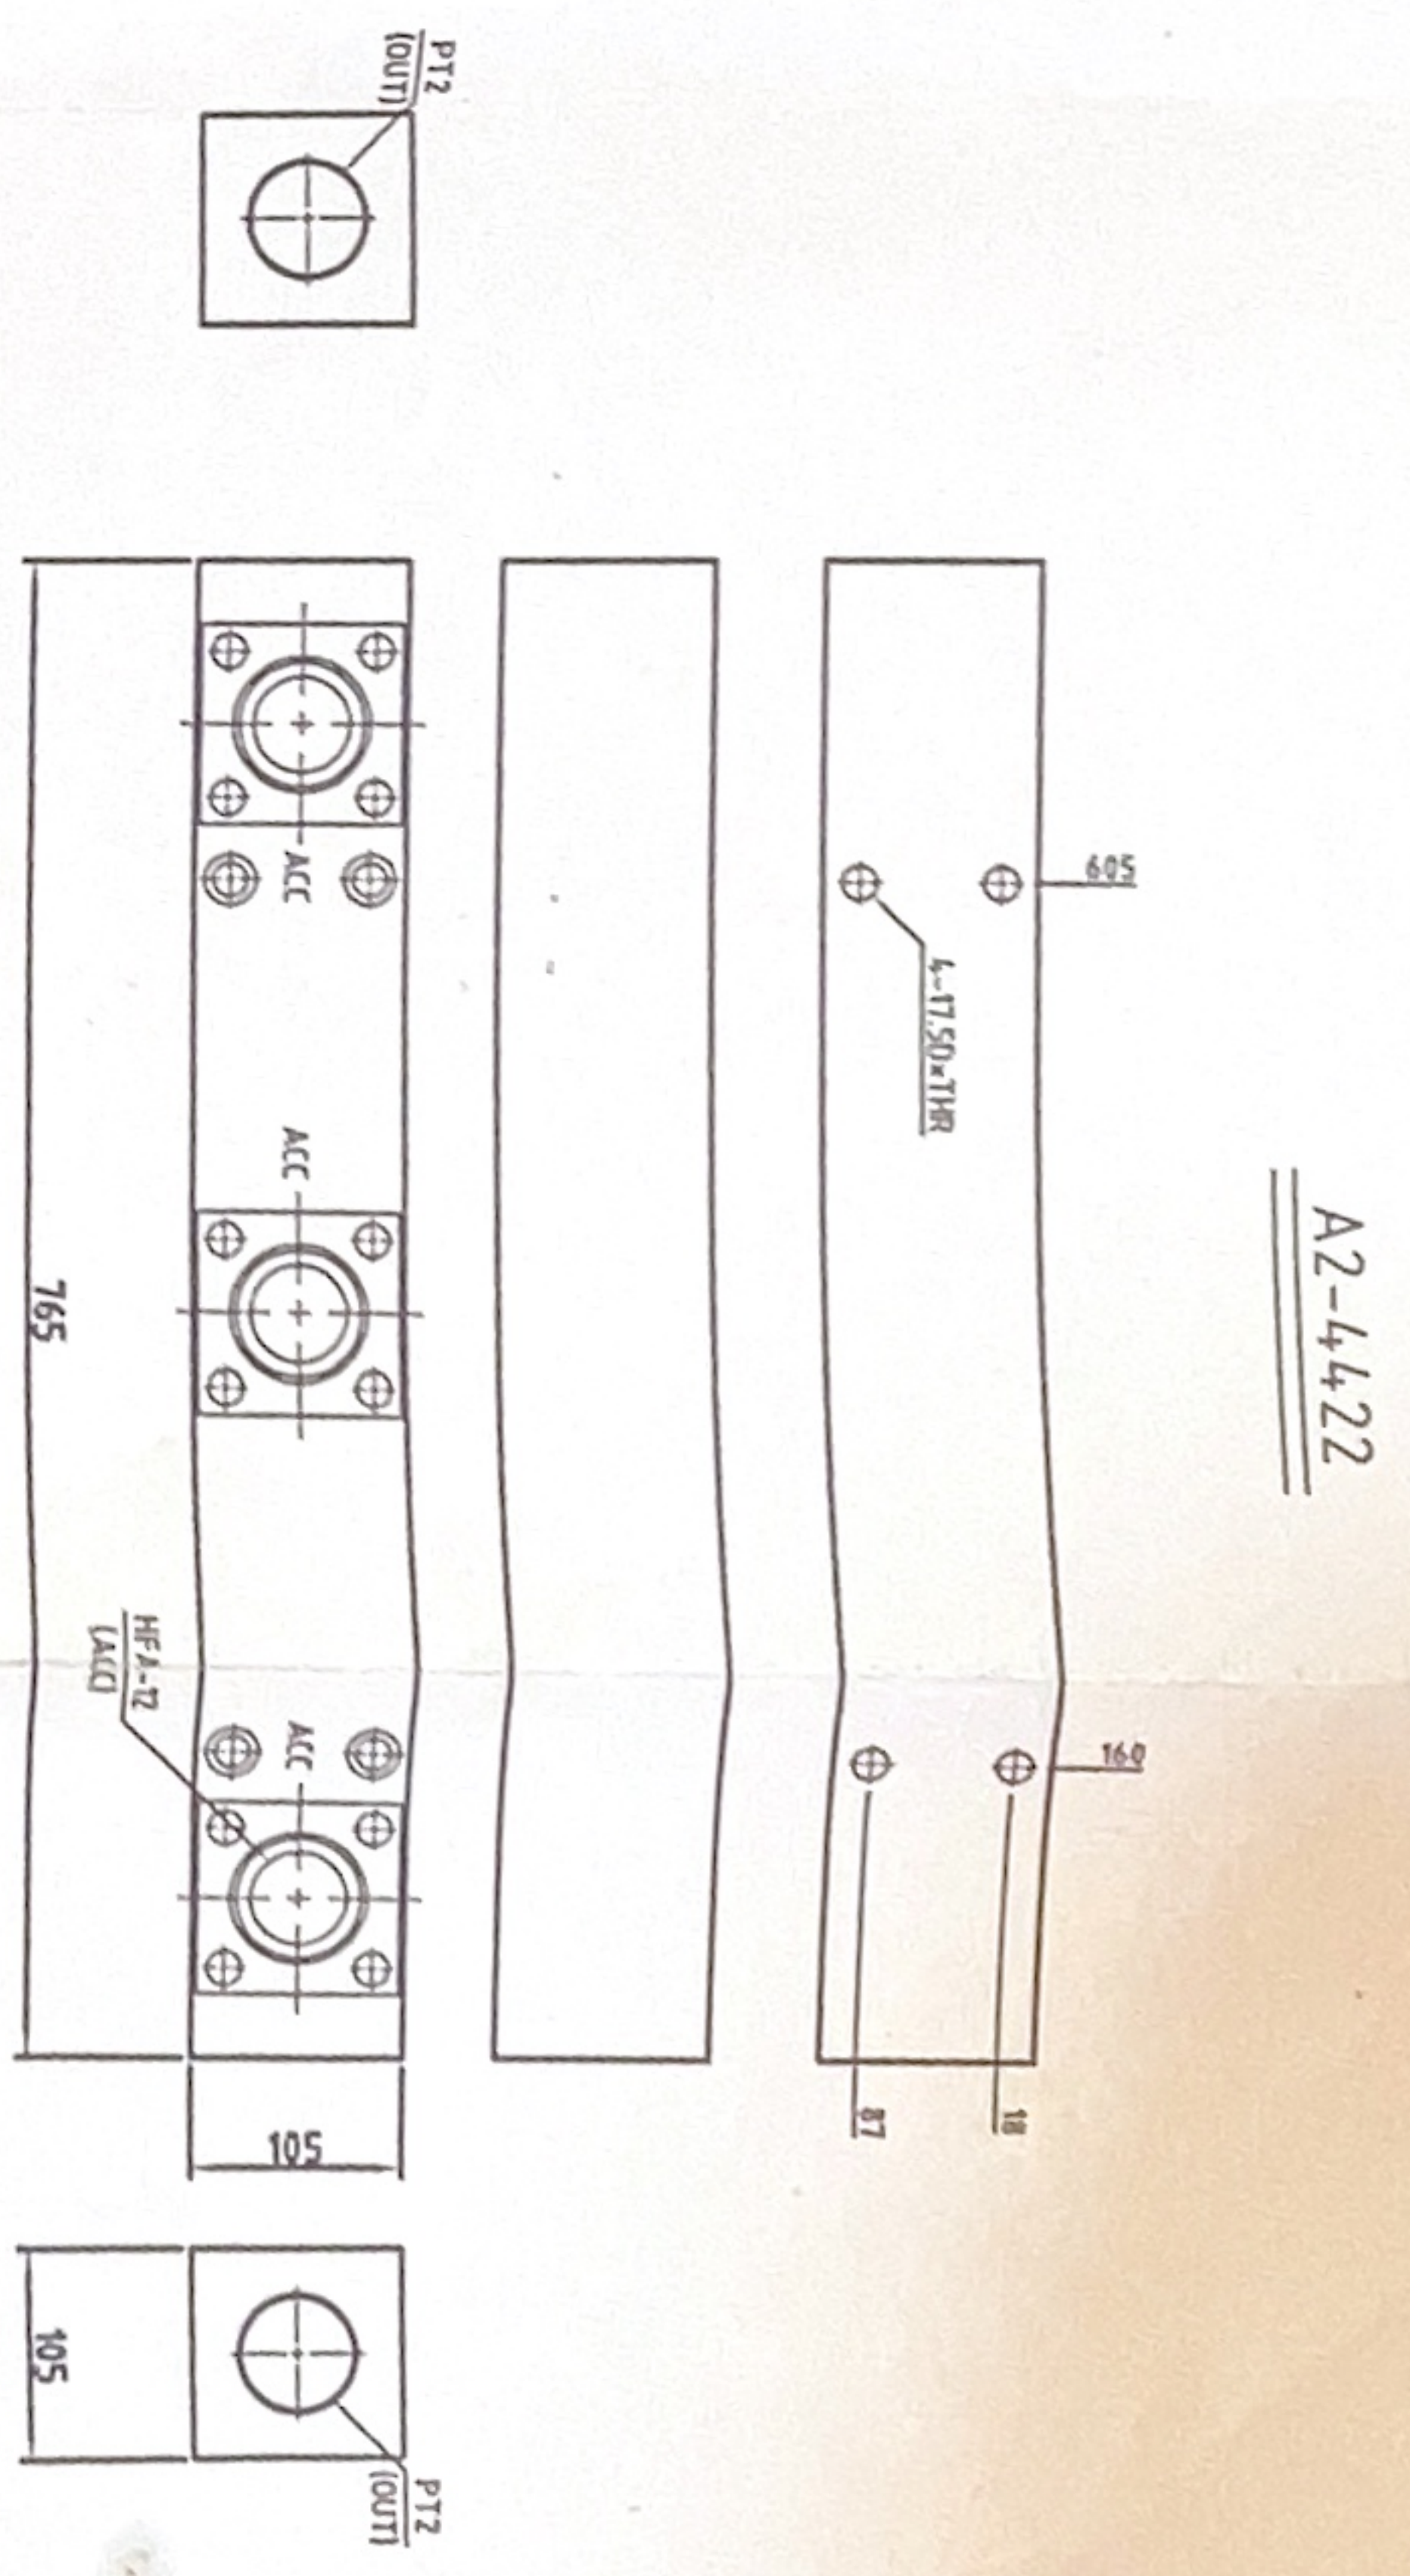


品名	型	式	數量	備註
1 通 閥	LGP-40		1	
2 比例壓力閥	KCG-3-250-D-Z-M-U-HL1-10		1	
3 通 閥	RD-08W-23-C-L		1	
4 通 閥	LE-20-B		1	
5 方向閥	DSG-01-283B		1	
6 通 閥	ST-02		1	
7 通 閥	RD-08W-23-A-L		1	
8 01 疊板	A3-6062		1	
9 通 閥	LE-20-B		1	
10 方向閥	DSG-01-283B		1	
11 通 閥	ST-02		1	
12 通 閥	RD-08W-23-A-L		1	
13 01 疊板	A3-6062		1	
14 通 閥	LGP-40		1	
15 比例壓力閥	KCG-3-250-D-Z-M-U-HL1-10		1	
16 通 閥	RD-08W-23-C-L		1	
17 通 閥	LE-20-B		1	
18 方向閥	DSG-01-283B		1	
19 通 閥	ST-02		1	
20 通 閥	RD-08W-23-A-L		1	
21 01 疊板	A3-6062		1	
22 通 閥	LE-20-B		1	
23 方向閥	DSG-01-283B		1	
24 通 閥	ST-02		1	
25 通 閥	RD-08W-23-A-L		1	
26 01 疊板	A3-6062		1	
27 止 回 閥	φ10-05		1	
28 止 回 閥	φ10-05		1	
29 止 回 閥	φ10-05		1	
30 止 回 閥	φ10-05		1	
31 止 回 閥	φ25-05		1	
32 止 回 閥	φ25-05		1	
33 止 回 閥	φ25-05		1	
34 止 回 閥	φ25-05		1	
35 止 回 閥	φ25-05		1	
36 止 回 閥	φ25-05		1	
37 止 回 閥	φ25-05		1	
38 止 回 閥	φ25-20		1	
39 止 回 閥	φ25-20		1	
40 通 閥	LE-20-B		1	
41 方向閥	DSG-01-282		1	
42 通 閥	MR-01-PP		1	
43 通 閥	LE-50-D-20		1	
44 BOLT 調整	LE-50		1	
45 通 閥	CVU-40-EFP1-B29-90-31		1	
46 方向閥	DSG-01-282		1	
47 通 閥	LE-32		1	
48 通 閥	NO-02		1	
49 通 閥	FCA-02C		1	
50 止 回 閥	φ6-05		1	
51 止 回 閥	φ6-05		1	
52 止 回 閥	φ25-20		1	
53 通 閥	LE-32-D-20		1	
54 方向閥	DSG-01-282		1	
55 通 閥	LE-40-D-05		1	
56 方向閥	DSG-01-282		1	
57 通 閥	LE-40		1	
58 通 閥	LE-32-B		1	
59 方向閥	DSG-01-282		1	
60 止 回 閥	φ6-05		1	
61 方向閥	DSHG-06-3C11		1	
62 比例壓力閥	EDG-01		1	
63 安全閥	RP-3A-20-A-L		1	
64 通 閥	FCA-02C		1	
65 止 回 閥	φ6-05		1	
66 止 回 閥	φ6-05		1	
67 通 閥	LE-20-D-20		1	
68 BOLT 調整	LE-20		1	

品名	型	式	數量	備註
69 通 閥	LE-20		1	
70 通 閥	LE-40-B		1	
71 方向閥	DSG-01-3C2		1	
72 通 閥	MR-01-PB-SS		1	
73 通 閥	LE-40-D-05		1	
74 方向閥	DSG-01-282		1	
75 通 閥	LE-40		1	
76 通 閥	LE-32-C-20		1	
77 方向閥	DSG-01-282		1	
78 通 閥	LE-32-D-05		1	
79 通 閥	LE-32		1	
80 方向閥	DSG-03-3C2		1	
81 止 回 閥	φ6-05		1	
82 止 回 閥	φ6-05		1	
83 止 回 閥	φ6-05		1	
84 止 回 閥	φ6-05		1	
85 止 回 閥	φ25-05		1	
86 止 回 閥	φ32-05		1	
87 通 閥	LE-20-C-20		1	
88 通 閥	LE-20-C-20		1	
89 方向閥	DSG-01-282		1	
90 通 閥	LE-25-8(補孔)		1	
91 比例壓力閥	KCG-3-250-D-Z-M-U-HL1-10		1	
92 通 閥	RD-08W-20-A-L		1	
93 通 閥	LE-20-C-20		1	
94 方向閥	DSG-01-282		1	
95 通 閥	LE-20		1	
96 方向閥	DSG-03-3C4		1	
97 止 回 閥	DSG-03-3C4		1	
98 止 回 閥	φ16-05		1	
99 方向閥	DSG-03-3C4		1	
100 止 回 閥	DSG-03-3C4		1	
101 止 回 閥	DSHG-06-3C2		1	
102 通 閥	MPW-03		1	
103 通 閥	MPW-03		1	
104 方向閥	DSG-01-284B		1	
105 通 閥	DSG-03-3C2		1	
106 通 閥	MRP-01		1	
107 通 閥	MPW-01		1	
108 通 閥	MPW-03		1	
109 方向閥	DSG-01-282		1	
110 通 閥	MPC-02W		1	
111 通 閥	A3-2590		1	
112 通 閥	LE-20-C-20		1	
113 通 閥	LE-20-C-20		1	
114 方向閥	DSG-01-282		1	
115 通 閥	LGP-25		1	
116 比例壓力閥	KCG-3-250-D-Z-M-U-HL1-10		1	
117 通 閥	RD-08W-20-C-L		1	
118 通 閥	LE-16-B		1	
119 通 閥	A3-7620		1	
120 方向閥	DSHG-04-282B		1	
121 通 閥	DSHG-04-3C10		1	
122 通 閥	FCA-06C		1	
123 止 回 閥	φ16-05		1	
124 止 回 閥	φ25-20		1	

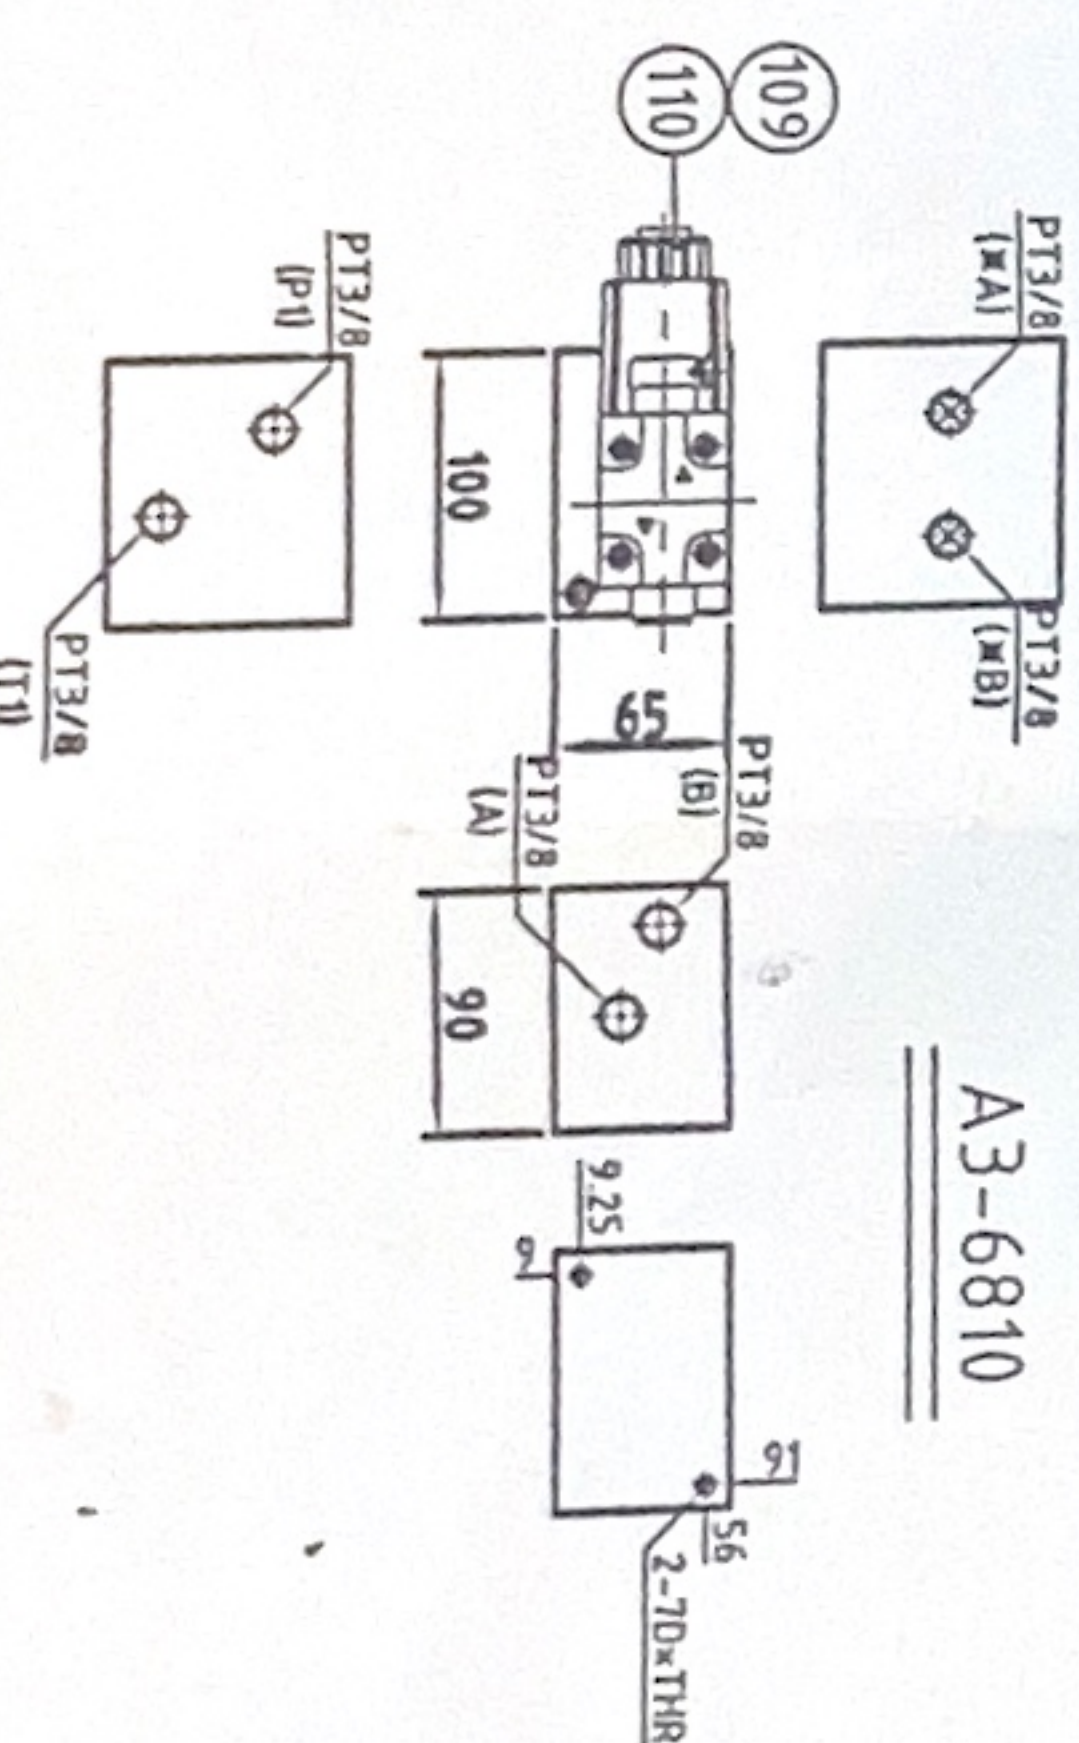

99.5.26

出圖

611

材料	數量	單位	備註
SS41	1	個	
比例	1	個	
製圖	1	張	
設計	1	張	
校核	1	張	
審核	1	張	
簽名	1	張	
日期	99.05.12		
客戶	850SOD		
項目	通流及開閉裝置		
圖號	CA3-15583-2		

勤榮機器工業股份有限公司